

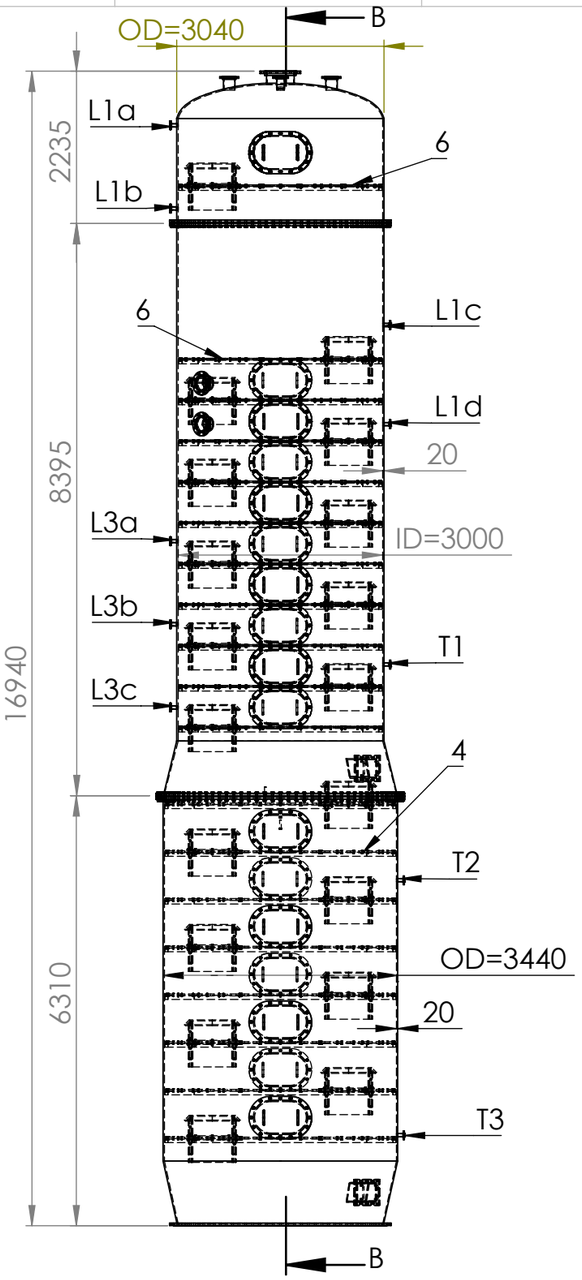


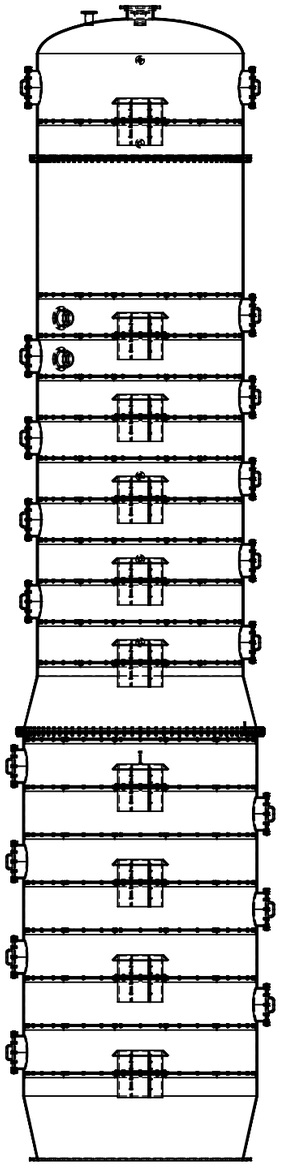

SECTION B-B
SCALE 1 : 90

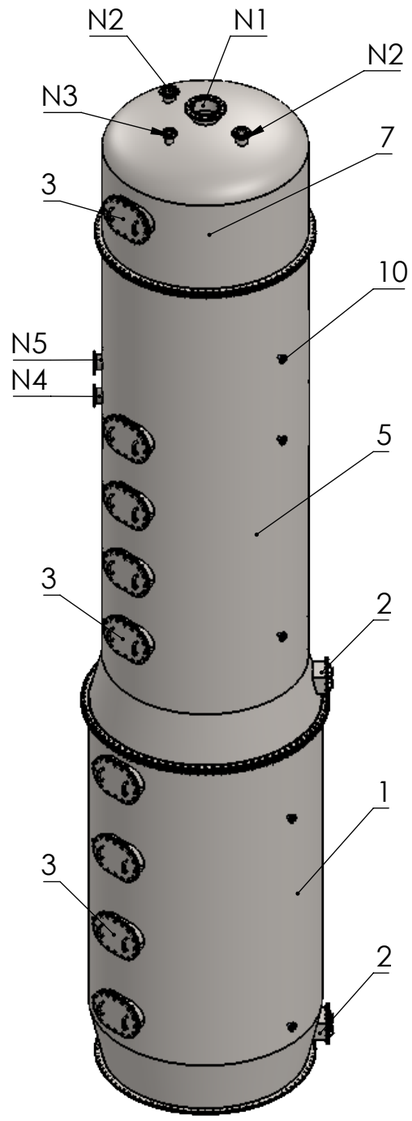

MARK	SIZE	CON.SIZE	FACING	DESGNATION
N1	400	ANSI 16.1 #150	RF	WASTED GAS OUTLET
N2	150	ANSI 16.1 #150	RF	WASHING NOZZLE
N3	100	ANSI 16.1 #150	RF	STEAM INLET
N4	200	ANSI 16.1 #150	RF	AMMONIA BRINE INLET
N5	200	ANSI 16.1 #150	RF	SPARE
L3a-c	40	ANSI 16.1 #300	RF	L.T TRANSFER
T1-3	40	ANSI 16.1 #300	RF	T.I
L1a-d	40	ANSI 16.1 #300	RF	L.G

NOT :
ALL WELD : EL 7018
ALL INLET COUTING : GLASS FLACK

PART NO.	DWG NO.	DESCRIPTION	MATERIAL	QTY
10	8502-DWG-400-MD-46	FLANGE	ST 52	10
9	-	Hex nut M24	ST 8.8	192
8	-	Hex Bolt M24 ×120	ST 8.8	192
7	8502-DWG-400-MD-35	PART 3	ST 52	1
6	8502-DWG-400-MD-29	BUBBLE CAP 2	ST 52	11
5	8502-DWG-400-MD-25	PART 2	ST 52	1
4	8502-DWG-400-MD-14	BUBBLE CAP 1	ST 52	8
3	8502-DWG-400-MD-09	MANHOLE 2	ST 52	18
2	8502-DWG-400-MD-05	MANHOLE 1	ST 52	2
1	8502-DWG-400-MD-01	PART 1	ST 52	1

UNLESS OTHERWISE SPECIFIED,
DIMENSIONS ARE IN MILLIMETERS
GENERAL TOLERANCES:DIN 7168
LINEAR: m ANGULAR: m
FREE WELDING TOLERANCE:DIN 8570

FINISH: DEBUR AND BREAK SHARP EDGES

FILE No:T4001-MAIN

DESCRIPTION:

MATERIAL: ST 52

WEIGHT:Kg

QTY. 1

A3

THIS DOCUMENT IS THE PROPERTY OF OWNER. IT IS CONFIDENTIAL AND ALL RIGHTS RESERVED BOTH OF OWNER AND AUTHOR. NO PART OF IT MAY BE DISCLOSED TO ANY THIRD PARTY, REPRODUCED, STORED IN ANY RETRIEVAL SYSTEM OR TRANSMITTED IN ANY FORM OR BY ANY MEANS WITHOUT THE PRIOR WRITTEN CONSENT OF OWNER.

REV.	ISSUE DATE	DESCRIPTION	OWNER'S ACTION	DWG BY	CHKD. BY	DEPT SUPR	PROJ. MGR
00	00/01/05	ISSU TO INSTRUCTION		S.BAGHBANI	R.DINZADEH	M.RASOOLMALI	M.ASGARIAN

OWNER: KAVEH GLASS INDUSTRY GROUP

PROJECT: KAVEH SODA CHEMICAL INDUSTRIES CO.

IFR IFC IFQ ASB

PROJ.NO: 8502

TITLE: CARBONITION TAWER

SCALE:

SHEET: OF:

DRAWING No: 8502- DWG-400-MD-00

REV. 00